

Weave House

Mix + Connect

Background

한국의 주거 환경은 대규모 아파트 단지와 빌라·다세대 중심의 저층 주거지 사이에서 이분화되어 있다. 제도와 시장은 소규모 필지의 개별 다세대주택과 대규모 아파트 단지는 양극의 개발 방식에 집중되어 있으며, 그 사이에서 주거의 질, 생활 인프라, 도시와의 관계를 함께 고려하는 중간 규모의 주거 모델은 충분히 만들어지지 못하고 있다.

이러한 구조는 공동생활의 조건을 두 방식으로 제한한다. 저층 주거지는 좁은 주거 면적, 주차 부족, 녹지와 공용시설의 부족으로 인해 주민이 집 밖에서 머물고 이웃을 만날 장소 자체가 부족하다. 반면 아파트 단지는 녹지, 주차장, 커뮤니티 시설 등 비교적 풍부한 인프라를 갖추지만, 시설의 존재만으로 주민 간의 자발적이고 지속적인 교류가 보장되지는 않는다.

그 결과 두 주거 유형 모두에서 이웃과 일상적으로 만나고 관계를 이어갈 기회는 제한되며, 서로 다른 주거 환경에 사는 주민들이 마주칠 공통의 장 역시 부족해진다. 주거는 개인의 집과 단지 내부의 편의시설을 제공하는 데 머무르고, 다양한 주민이 함께 생활하고 관계를 확장할 지역의 기반은 충분히 형성되지 못한다.

따라서 우리는 저층 주거지의 도시적 개방성과 아파트의 생활 인프라를 결합하는 중간주택을 제안한다. 열린 통로와 마당은 골목·시장·건물을 잇는 일상적 보행과 체류를 만들고, 공유시설·지역 프로그램·공동운영은 그 만남을 지속적인 활동으로 이어준다. 이를 통해 세대·소득·가구 형태가 다른 주민이 함께 살아갈 수 있는 조건을 만들고 (Mix), 입주민·기존 주민·지역 상인이 생활권 안에서 관계를 이어갈 수 있는 기반을 마련한다(Connect).

Concept & Vision



WEAVE

WEAVE는 베를 위에 서로 다른 색의 날실을 나란히 겹고, 그 사이를 반복해 가로지르는 씨실로 하나의 직물을 만드는 방식이다. 이 프로젝트에서 날실은 서로 다른 세대·소득·가구 형태·주거 방식과 일상 활동을, 씨실은 이들을 반복적으로 만나게 하는 공간·프로그램·운영을 뜻한다. WEAVE는 다양한 삶이 한곳에 공존하도록 섞고(Mix), 그 관계가 일상 속에서 지속되도록 잇는(Connect) 중간주택 모델이다.



Mix | 함께 살아갈 조건 만들기

Mix는 서로 다른 이용자를 한 장소에 모으는 데 그치지 않고, 다양한 주민이 같은 생활권 안에서 함께 거주할 수 있는 조건을 만드는 일이다. 스튜디오형부터 2베드룸형까지 다양한 주택형을 마련하여 1인 가구와 다인 가구, 서로 다른 생애 단계의 가구를 수용한다. 제한지분과 공공지원 구조는 주거 접근성이 필요한 가구도 안정적으로 거주할 수 있도록 뒷받침하고 일반 조합원, 공공지원 조합원, 재정착 조합원은 특정 주택형이나 구역에 분리하지 않고 배정한다. 주거만 단일하게 배치하는 대신, 1층의 상업·가변 공간과 마당을 통해 주거, 지역 생활, 상업 활동이 한 부지 안에서 공존하도록 한다. 이를 통해 다양한 사람과 활동이 함께 살아갈 물리적·사회적 기반을 만든다.



Connect | 일상 속 관계를 이어가기

Connect는 일화성 행사를 늘리는 것이 아니라, 매일의 이동과 짧은 체류, 반복적인 활동 속에서 관계가 이어지도록 만드는 방식이다. 상시 개방 보행축은 골목과 시장을 연결하고, 그 흐름은 마당과 1층 가변 공간으로 이어진다. 별도의 행사가 없는 날에도 통행, 짧은 체류, 시장 이용이 자연스럽게 지속되도록 하며, 주거 출입은 공공 동선과 구분하여 거주자의 프라이버시를 보호한다. 시장 상인의 팝업과 공동행사, 주민 주도 프로그램은 입주민·인근 주민·지역 상인이 함께 이용하고 운영에 참여하는 계기를 만든다. 주차·상업·대관에 서 발생하는 순수익은 공동공간의 운영과 입주민의 주거비 부담 완화에 환원하여, 공간의 공공성과 관계의 지속성을 함께 뒷받침한다.

Vision

WEAVE는 저층 주거지의 골목과 시장이라는 기존 생활자원을 바탕으로, 아파트와 다세대주택 사이에 새로운 중간주택 선택지를 제안한다. 공간과 운영을 통해 더 풍부한 일상을 만드는 '살고 싶은 주거'와 제한지분·공공지원·수익 환원을 통해 접근성과 장기 거주 안정성을 높이는 '살 수 있는 주거'를 함께 만드는 모델이다.

Site

안정적인 주택 공급의 필요성

관악구 신사동은 1인 세대 비율이 높은 생활권이다. 2026년 7월 기준 전체 14,836세대 중 1인세대는 10,554세대로 71.1%를 차지해, 소규모 가구의 주거 수요가 두텁게 형성되어 있다. 관악구의 월세 가구 비중은 40.6%로 서울 전체의 28.1%보다 높다. 최근 2년간 주거불안 경험 비율도 관악구 8.3%, 서울 3.8%이며, 이사·재계약 과정에서 보증금 부족을 경험한 비율은 관악구 6.2%, 서울 2.3%로 나타났다.

이는 주거비 대응 여력이 제한된 가구가 안정적으로 거주할 수 있는 주택 공급의 필요성을 보여준다. (출처: 행정안전부 주민등록 인구통계, 2026년 7월, 서울연구원 『2024 서울시 주거실태조사 조사보고서』)

공공 생활공간의 부족

신사동은 소규모 필지 위에 다세대·다가구주택과 근린생활시설이 밀집한 저층 주거지다. 지역 내 개별 공원시설은 존재하지만, 대상지와 관악신사시장이 맞닿는 구간에는 주민과 시장 이용자가 일상적으로 머물 수 있는 광장·마당형 공공공간이 형성되어 있지 않다. 골목은 주로 이동 통로로 이용되며 휴식·체류·교류를 수용할 공간은 부족하다. 공공적 생활공간이 부족한 동시에 소규모 필지가 연속되어 있다는 점은 통합개발 대상지로서의 가능성을 보여준다. (현장 답사 및 대상지 주변 공간구조 분석)

관악신사시장과 지역경제

대상지와 직접 맞닿은 관악신사시장은 100개 점포로 구성된 골목형 전통시장으로, 주민의 일상생활과 지역경제를 지탱하는 기반이다. 현장 답사 결과 시장 진입부는 주변 골목과 유사한 폭으로 형성되어 있으며, 시장과 주거지 사이의 전면·체류 공간도 부족하다. 대상지는 시장과 연속적으로 접해 있어 주거지의 일상적인 이동과 활동이 시장 및 주변 로컬 비즈니스와 직접 연결될 수 있다는 입지적 가능성을 가진다. (관악구청 전통시장 현황, 현장 답사)

필지 선정

이러한 지역 조건을 종합하여 관악신사시장과 맞닿아 있고 신대방역에서 도보 약 7~10분 거리에 위치한 관전로15길 일대의 15개 필지를 대상지로 선정하였다. 대상지로는 관전로15길을 기준으로 남측 필지 8곳(Site A: 총 1,348.20m²)과 북측 필지 7곳(Site B: 1,265.56m²)을 통합해 총 대지면적 2,613.76m²에 달하는 2개의 필지로 재편하였다. 이곳은 안정적인 주택 공급의 필요성, 저층 필지의 통합 가능성, 공공적 생활공간의 부족, 관악신사시장과의 직접적인 접점, 역세권 접근성이 함께 나타나는 장소로서 WEAVE 중간주택 모델의 대상지로 선정하였다.

Proposal



Public-Private Gradient

본 프로젝트의 공간은 공공성의 정도에 따라 '완전 공공 개방', '준공공 공유 공간', '입주민 전용 공간'의 3단계 위계로 구성된다. 이를 통해 개방적인 도시 공공성과 거주자만의 쾌적한 주거성을 균형 있게 확보한다.

완전 공공 개방 공간
주택과 주변의 경계를 허물고 골목·시장·부지를 하나의 보행 흐름으로 연결한다. 주 이용자: 보행자, 시장 이용객, 지역주민, 입주민 공간: 상시 개방 보행축, 시장 연결부, 1층 상업공간

준공공 공유 공간
공공 영역과 주거 사이에 완충지대를 형성하여 지역과 입주민을 잇는다. 주 이용자: 입주민, 지역주민, 시장 상인, 방문객 공간: 중앙 마당, 1층 가변형 공간

입주민 전용 공간
외부 동선과 주거를 분리하여 거주자의 일상과 프라이버시를 보호한다. 주 이용자: 입주민 및 입주민 동반 방문객 공간: 주거 유닛, 입주민 공동생활공간, 층별 복도·발코니



Unit Mix & Count

Site B						Site A						
Building 2		Building 1			Level	Building 2 (shorter)			Building 1 (taller)			
원룸 B	투룸 B	원룸 A	원룸 B	투룸 B		원룸 A	원룸 B	투룸 B	원룸 A	원룸 B	투룸 A	투룸 C
40.7m²	63.24m²	31.5m²	40.7m²	63.24 m²		31.5m²	40.7m²	63.24m²	31.5m²	40.7m²	56.27m²	64.7m²
				2	8				3		1	
		4			7				3		1	
		4			6				3		1	
		3			5				3			
	2		4		4	4				3		1
4			4		3		4			3		1
	2		4		2			2		3		1
4	4	11	12	2	Total	4	4	2	12	9	3	3

원룸	56세대
투룸	14세대
전체 (A+B)	70세대

본 프로젝트의 주거 유닛은 대상지의 높은 1인 가구 비율과 청년·신혼부부 등 다양한 가구 형태를 수용할 수 있도록 층원율 56세대와 투룸 14세대, 총 70세대로 구성된다. 여기에 전체 세대수의 15%에서 35% 범위를 공공지원 협동조합형 주거로 배정하여, 초기 입주 부담을 낮추고 장기적으로 안정적인 거주가 가능한 지속 가능한 주거 환경을 마련한다.


- 유닛
- 코어
- 가변형 공간
- 상업 공간
- 커뮤니티 공간
- 주차

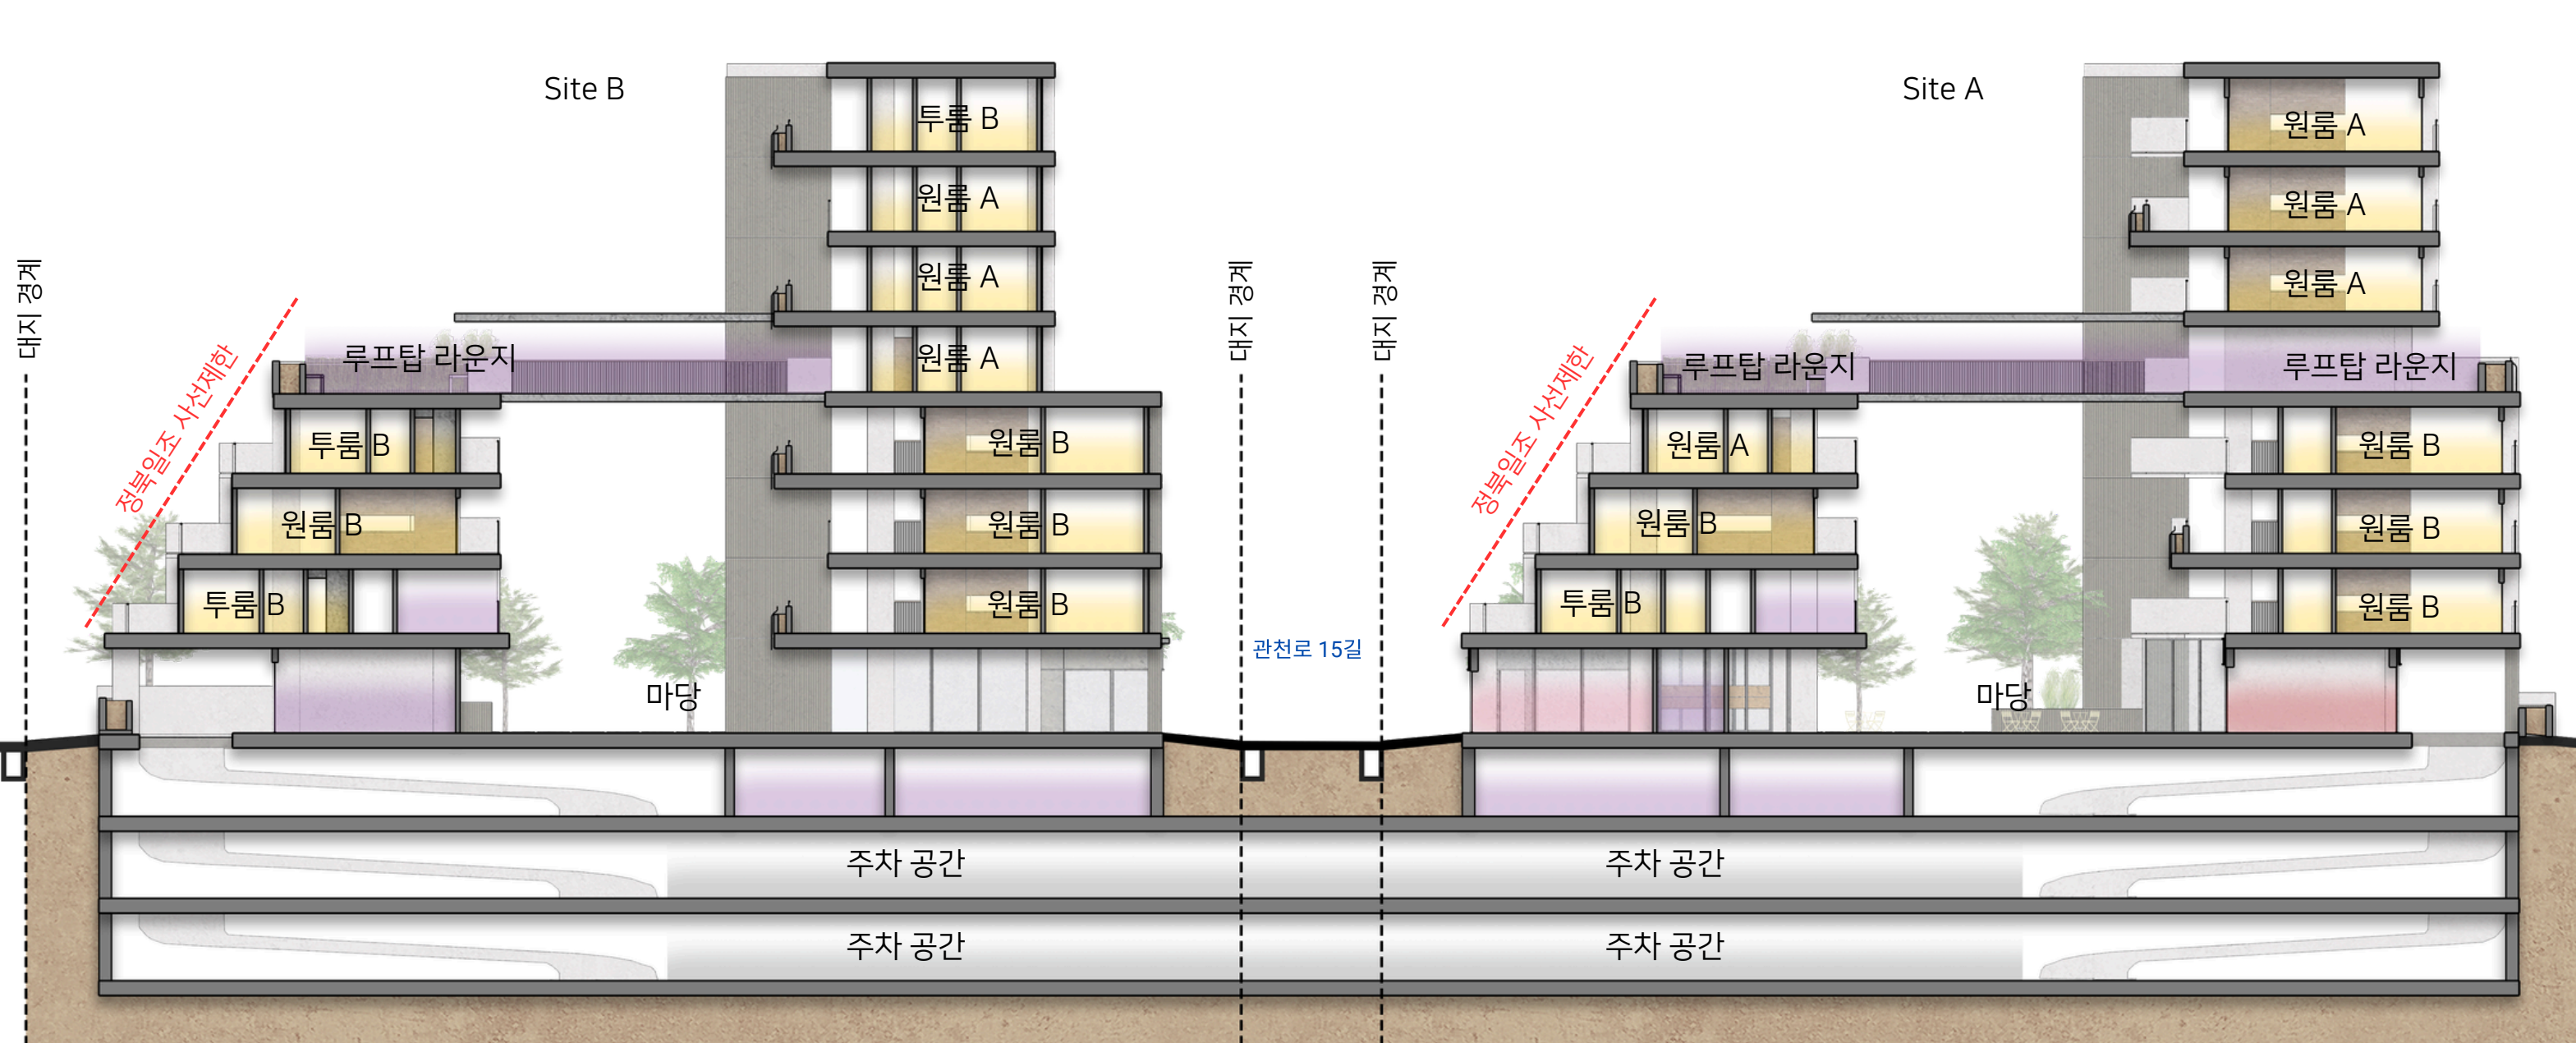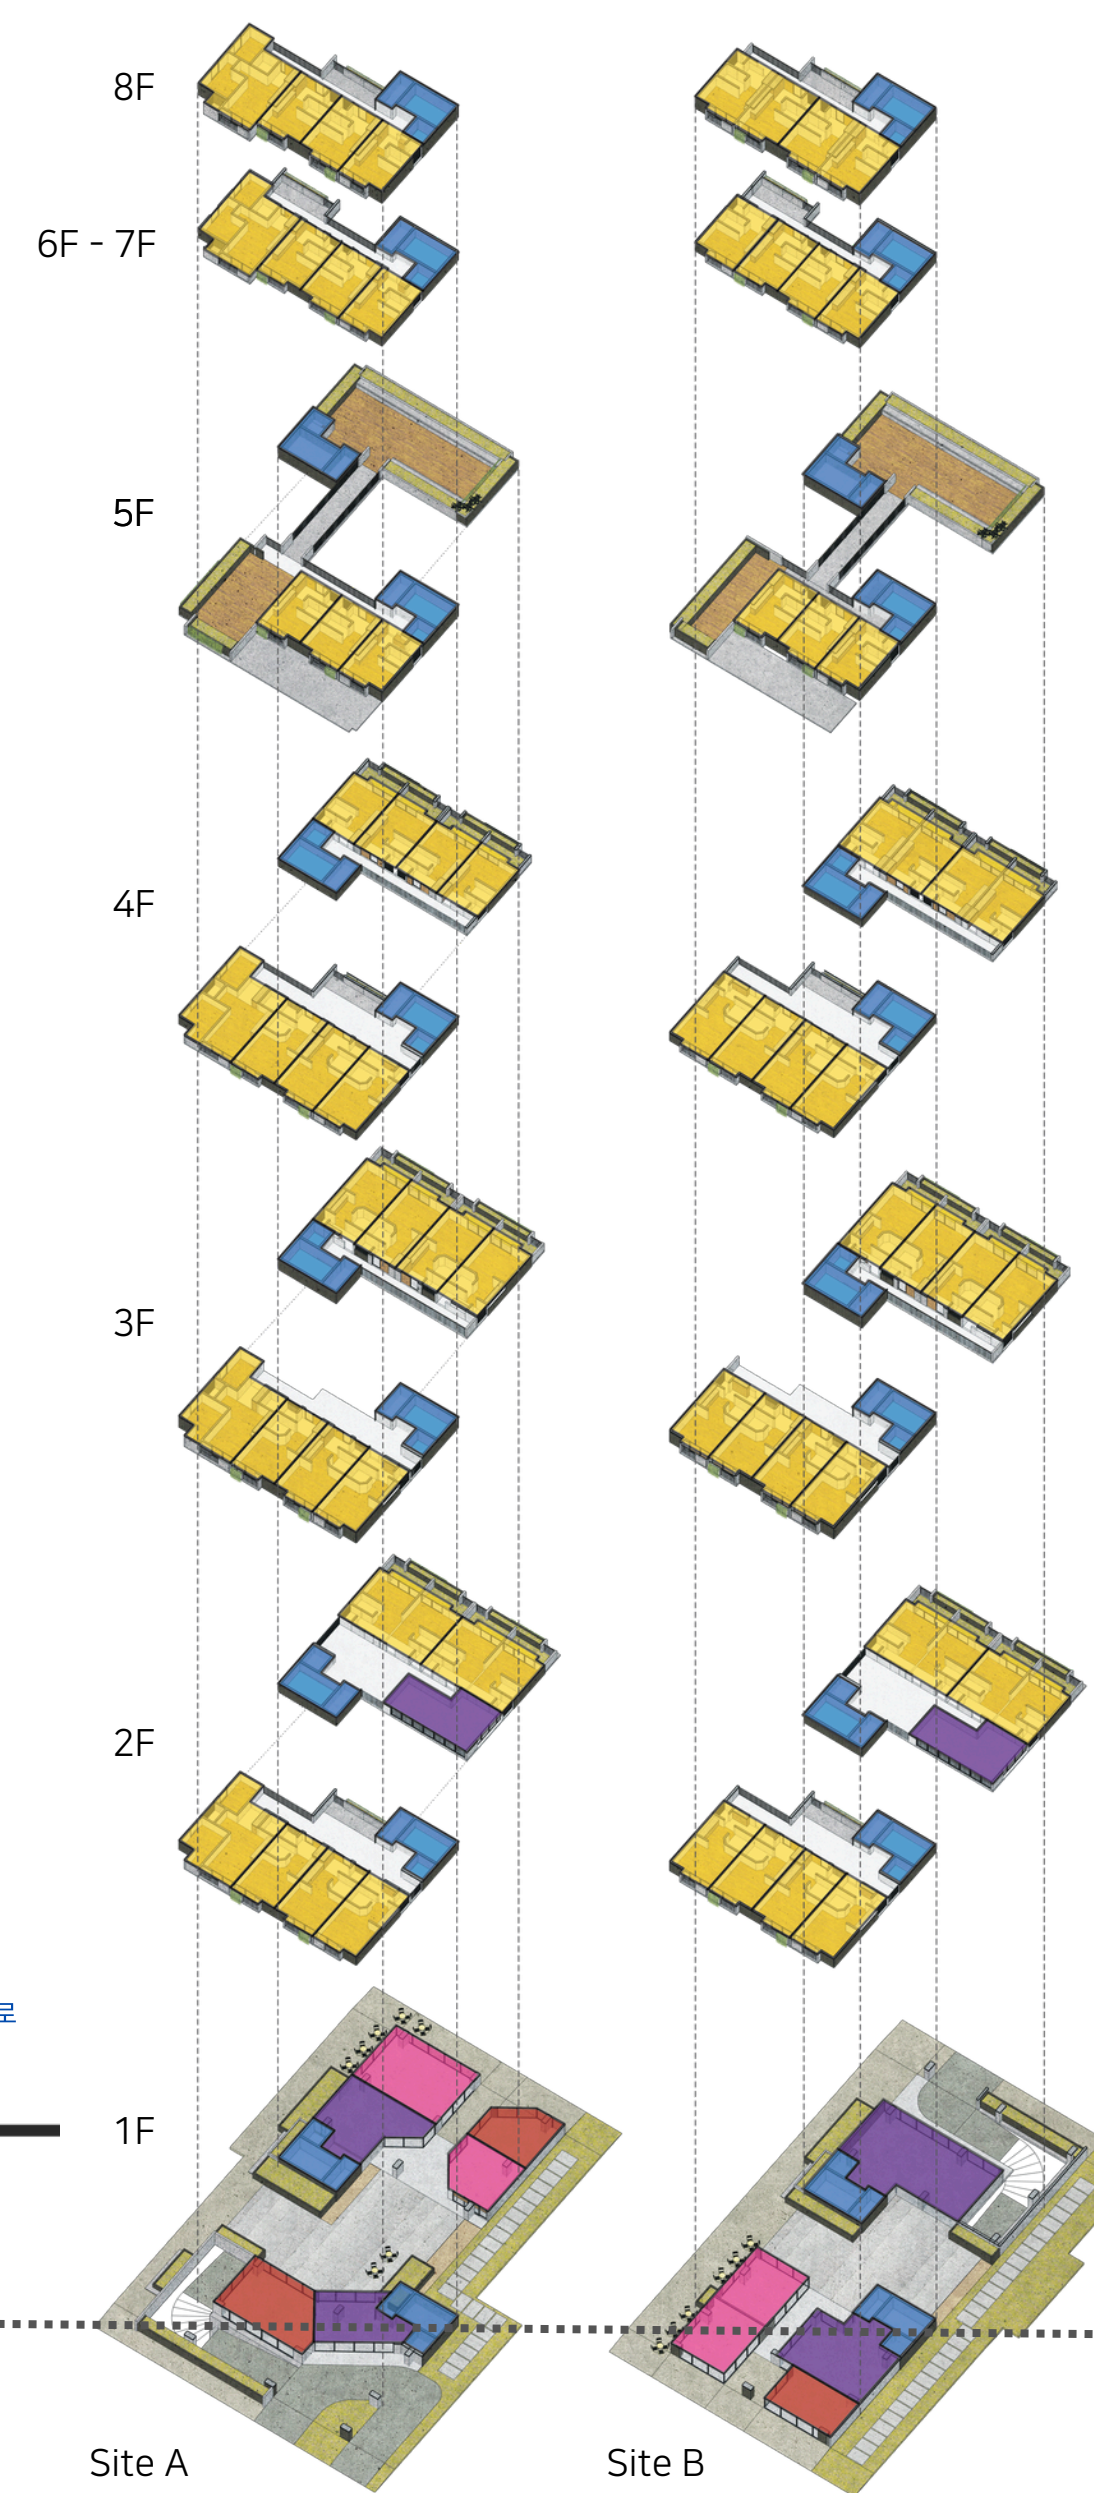

Program

완전 공공 개방 공간

골목과 시장, 마당, 1층 공간을 연결하고 항시 개방하여 자연스러운 통행과 짧은 체류가 이어지는 열린 보행환경을 조성한다. 상시 개방 보행 축은 기존 골목의 흐름을 부지 안으로 연장하여, 건물 배치로 끊길 수 있는 양측 골목을 연결하는 통로로 작동한다. 입주민은 물론 지역주민과 시장 이용객도 자유롭게 이용할 수 있다.

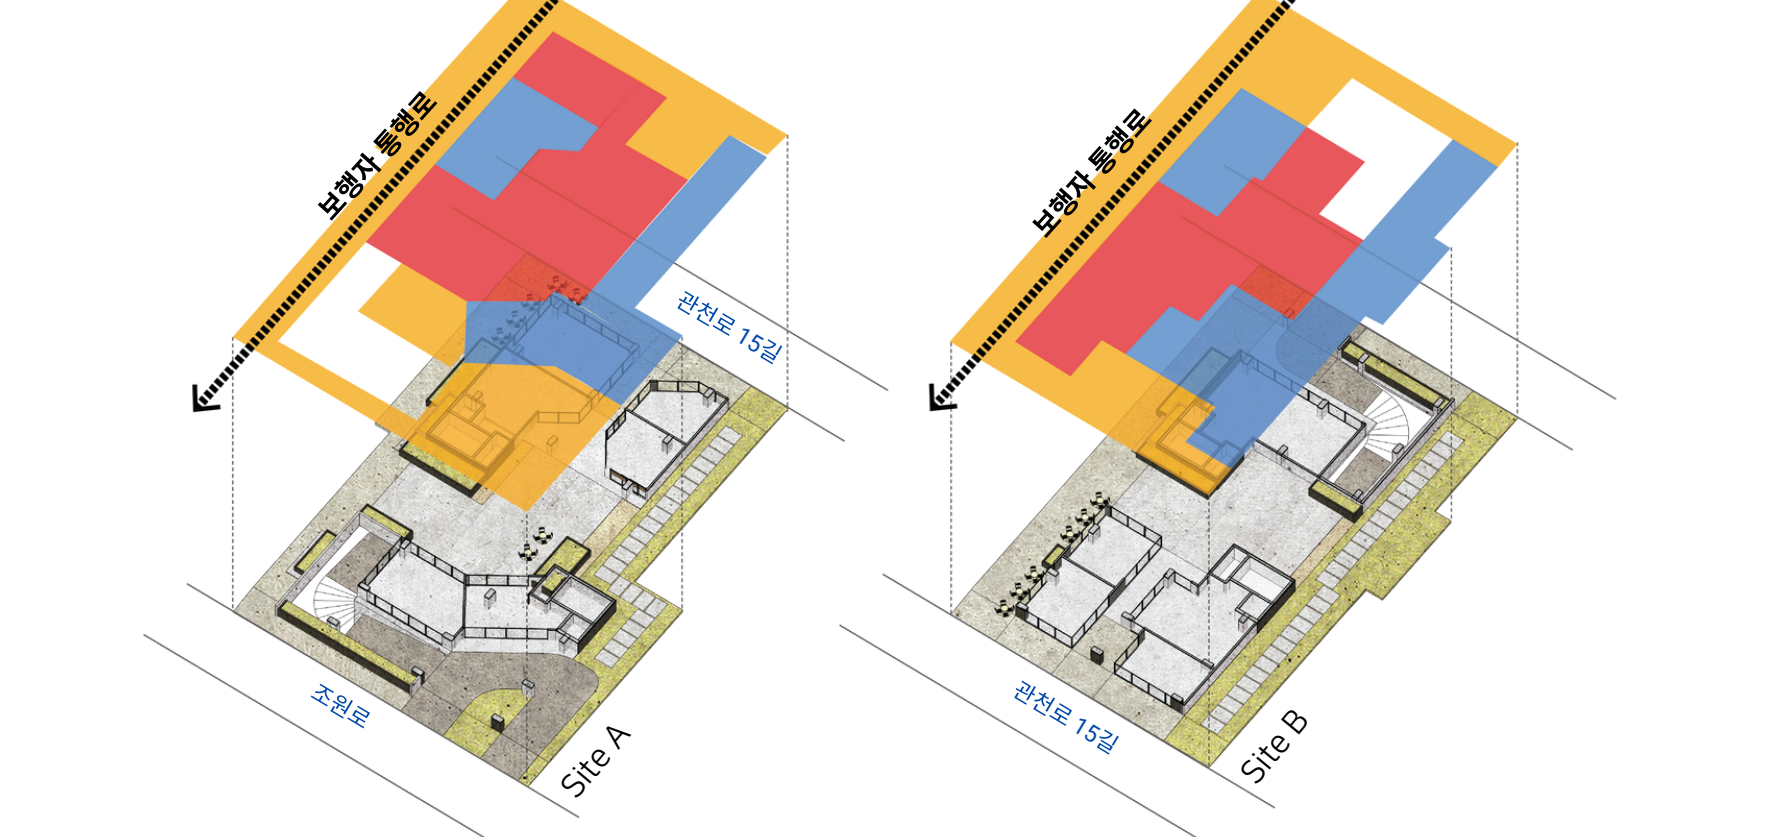

보행축에 면한 1층 상업공간은 출입구와 투명한 입면을 보행축 방향으로 배치하여 활성 가로면을 형성한다. 이를 통해 보행자가 내부 활동을 인지하고 자연스럽게 접근할 수 있도록 한다. 보행축에는 충분한 조명과 열린 시야를 확보하는 한편, 주거 출입구는 공공 동선과 분리한다. 이를 통해 주택과 주변 지역의 경계를 낮추면서도 거주자의 안전과 프라이버시를 보호하고, 주택을 동네 보행체계에 연결된 생활공간으로 만든다.

준공공 공유 공간

중심 마당과 1층의 가변형 공간은 주민과 지역 커뮤니티의 의견을 반영하되, 전문 운영 인력의 큐레이션을 통해 정기적으로 서로 다른 프로그램을 운영한다. 이 공간은 영화 상영, 공동 식사, 소규모 공연이나 워크숍 등 지역 커뮤니티가 함께 모일 수 있는 공동 행사의 장소로 활용된다. 또한 시장 상인과 로컬 비즈니스의 팝업 행사도 유치한다. 주민과 지역 주민에게는 집 가까이에서 다양한 지역 브랜드를 경험하고 행사 혜택을 누릴 기회를 제공하며, 참여 상인과 브랜드에는 홍보와 함께 자신이 속한 지역 커뮤니티의 고객 반응을 직접 확인할 수 있는 장이 된다. 단순히 행사를 위한 대관 공간이 아니라, 사람들이 함께할 수 있는 장소와 콘텐츠 (즉, 기회) 를 지속적으로 제공하는 생활권의 문화적 거점이다.



주기적으로 다른 프로그램이 열리는 이 공간은 방문할 때마다 작은 새로움과 설렘을 기대할 수 있는 장소가 된다. 입주민과 지역 주민 모두에게는 평소 애용하던 이웃이나 지역의 아는 사람을 다시 만나는 일상의 접점이 되며, 시장에 가거나 집으로 돌아가는 길에 잠시 들러 행사와 마당을 경험하는 과정 자체가 생활 속의 소소한 즐거움이 된다. 입주민에게 이 공간은 단순히 외부에 개방된 시설이 아니라, 주거의 일상에 문화·교류·휴식을 더하는 건물 내부의 공동생활공간이다. 입주민은 운영 규칙과 프로그램 구성에 의견을 내고, 지역 주민의 수요와 함께 반영하여 이 공간이 자신의 생활과 동네에 필요한 방식으로 지속되도록 참여한다. 또한 주차장 이용료, 대관·행사 등 공간 운영에서 발생한 수익은 공간 유지관리와 공동체 프로그램에 우선 재투자하고, 입주민의 공용관리 부담을 줄이거나 공동의 혜택으로 환원한다. 이를 통해 입주민, 지역 주민, 지역 상인이 같은 공간에서 경험을 나누고 관계를 자연스럽게 이어가며, 단절된 지역의 관계망을 회복한다.

입주민 전용 공간

외부와 분리된 안전하고 아늑한 환경에서 거주자의 일상과 프라이버시가 보호되도록 계획한다. 독립적인 주거 유닛과 전용 출입 동선을 마련하고, 공공·준공공 공간에서 주거 영역으로 들어갈수록 접근 권한이 단계적으로 제한되는 공간 체계를 적용한다.



주거동 내부에는 주거 유닛과 함께 층별 복도 발코니, 입주민 전용 아메니티, 루프탑 라운지 등 생활에 밀착된 공유공간을 배치한다. 이 공간들은 개별 주거에서 수용하기 어려운 휴식과 공동 생활을 지원하고, 입주민이 머물거나 이웃을 만날 수 있는 주거의 확장 공간을 제공한다. 이를 통해 독립적인 생활을 보장하면서도 입주민 간의 자연스러운 교류와 유대가 형성될 수 있도록 한다.

주차장

본 개발에서는 필지 통합후 지하 3층까지 개발 구성을 하여 입주민과 외부 주민이 함께 쓰는 주차 81면을 구성하였다. 낮에는 시장 및 프로그램 방문객에게, 야간에는 인근 주민에게 개방하는 '시장 공유형'으로 운영하며, 주차·상업·공간 대관을 통해 발생하는 순수익은 단지 운영비와 입주자 주거비 부담을 완화하는 데 활용한다.